


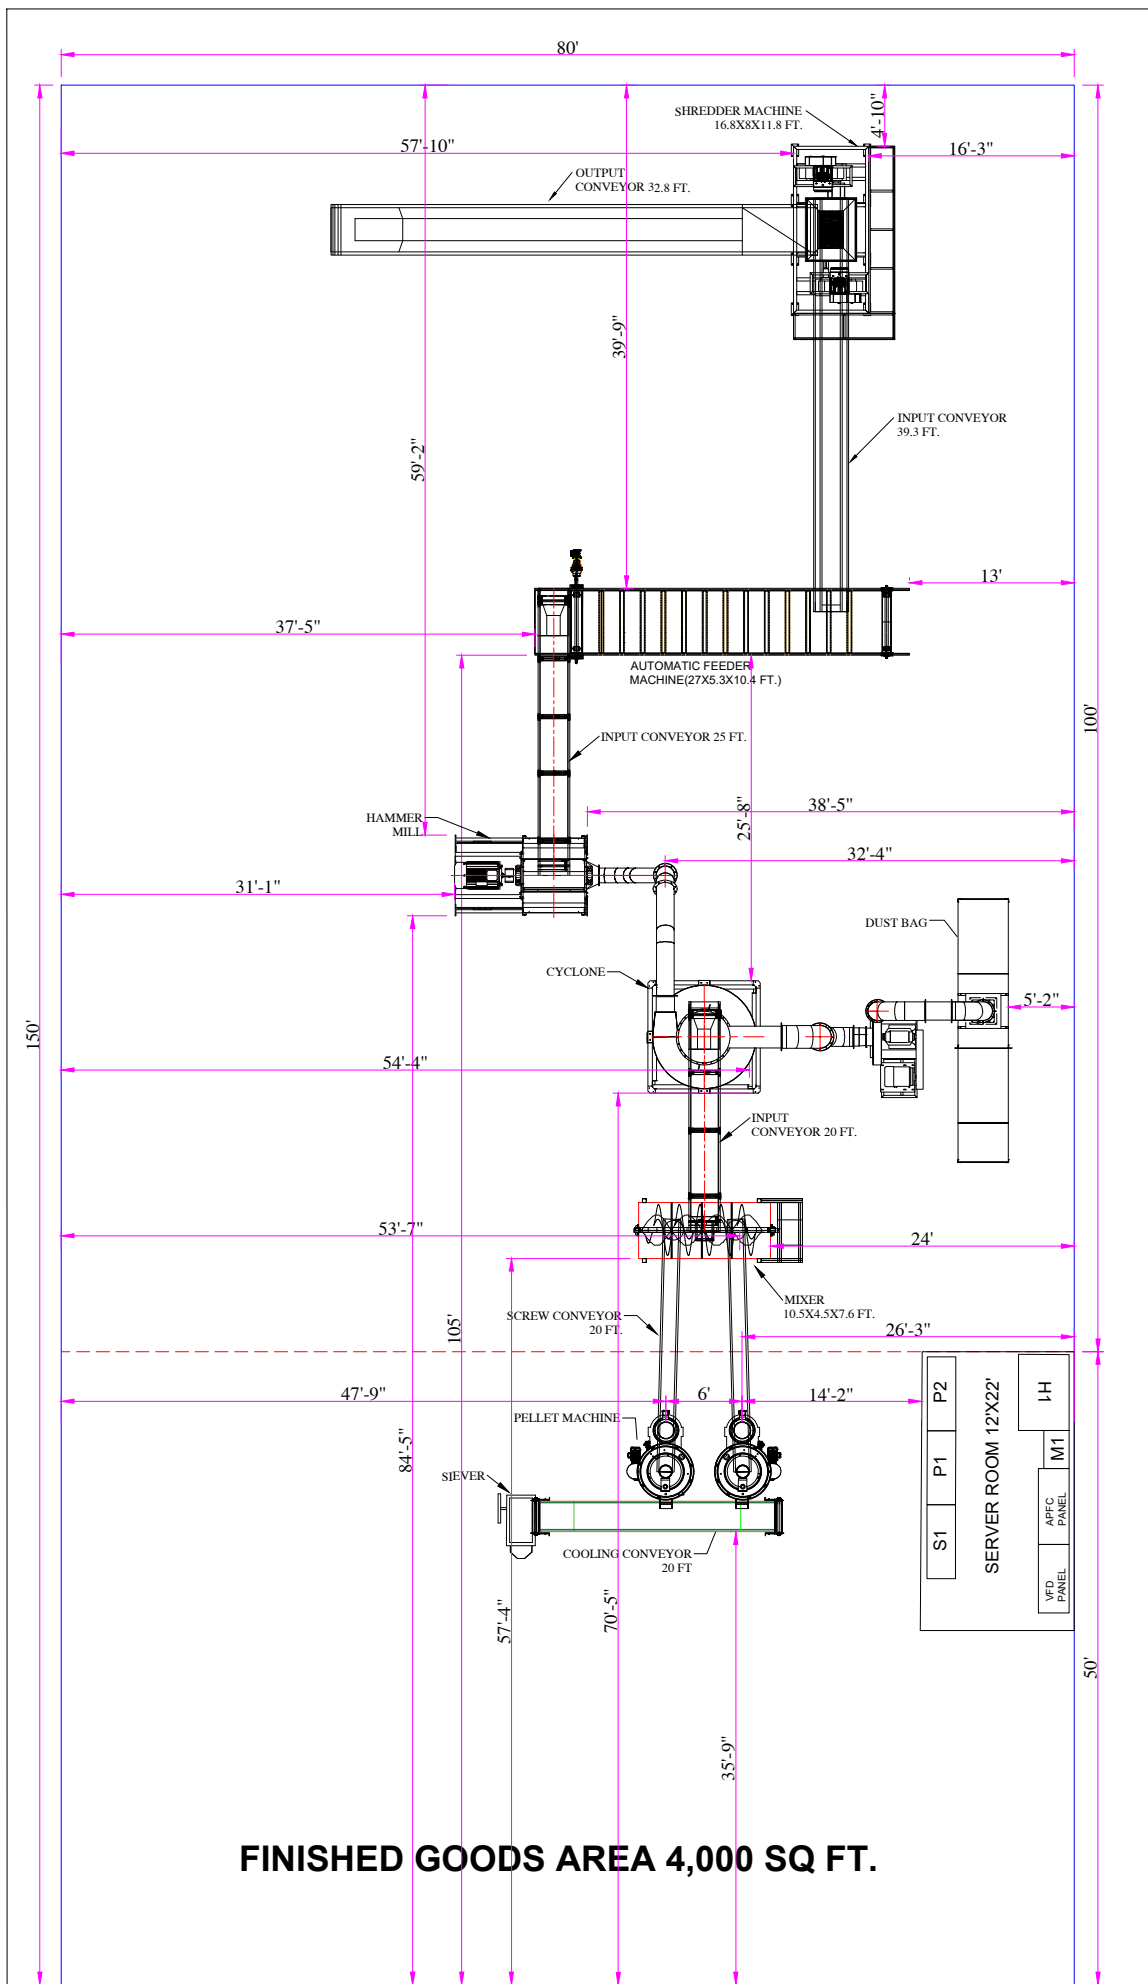

1. 6" (150MM) RCC TRIMIX FLOORING
2. REQUIRED SHED AREA 12,000 SQ FT.
3. REQUIRED SHED HEIGHT 35 FT.

CLIENT	XXXXXXXXXX	DATE	08-06-2026	 GATTUWALA Energy Solutions Private Limited	GATTUWALA ENERGY SOLUTIONS PVT.LTD. OFFICE: PEARL BEST HEIGHT 2, 1002 & 1003, NETAJI SUBHASH PLACE, PITAMPURA DELHI-110034 www.gattuwalla.com
		DRAWN	AMIT KUMAR		
		CHECKED BY	-		